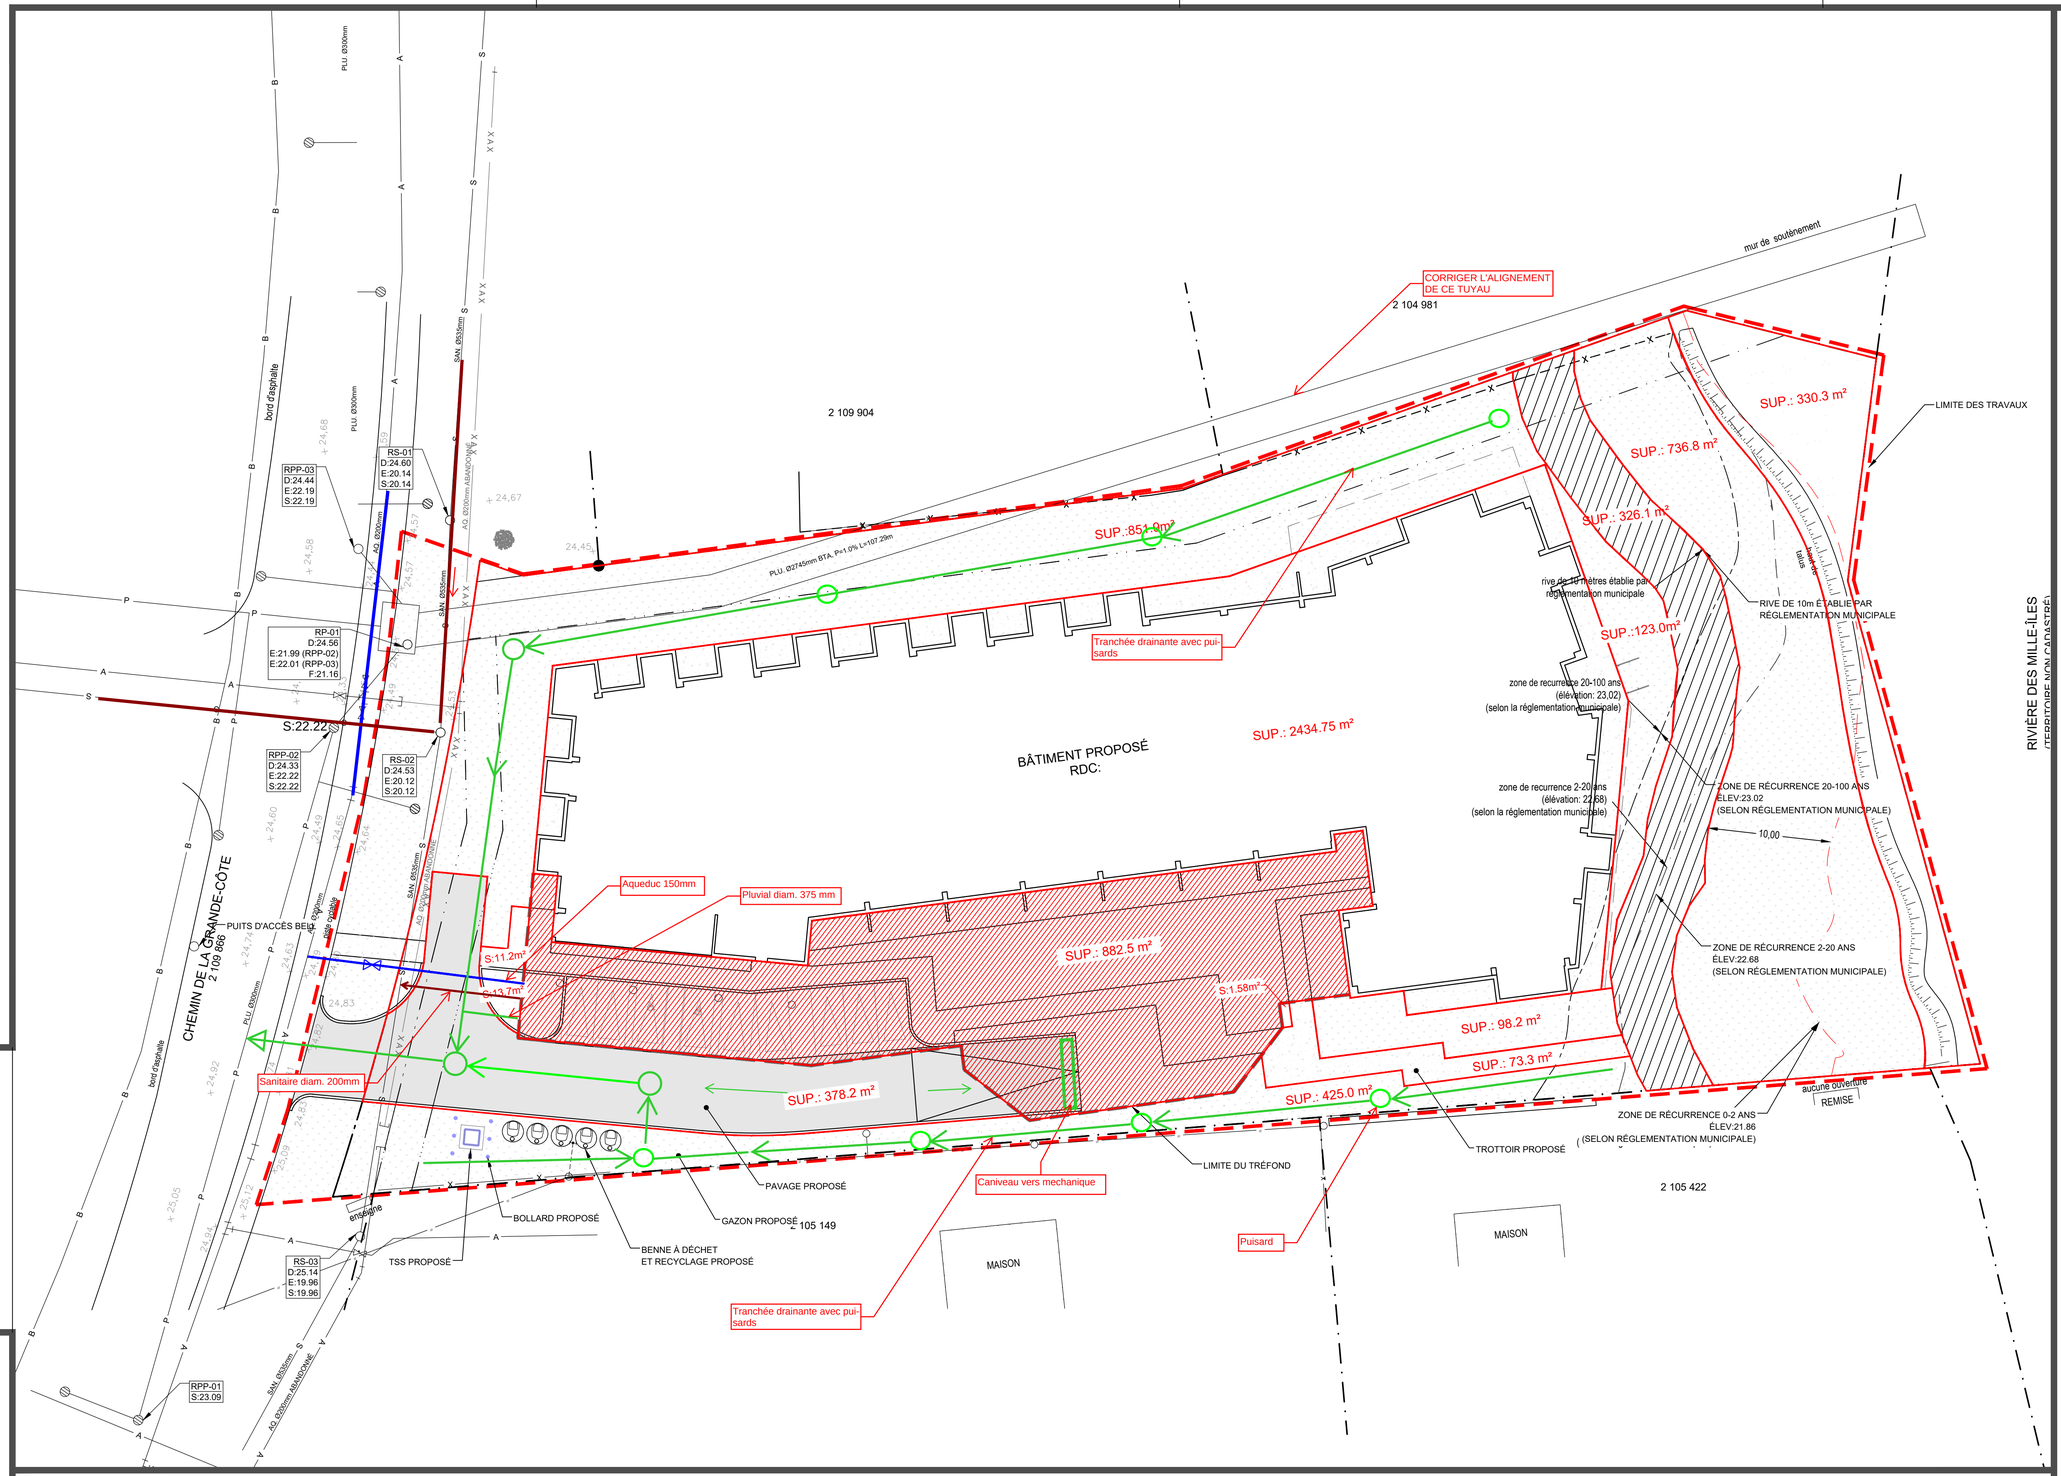


contrat no.
plan no.

MÉTRIQUE
TOUTES LES UNITÉS DE MESURE SONT DANS LE SYSTÈME INTERNATIONAL

NOTES
NE PAS UTILISER CE PLAN POUR CONSTRUCTION.

NOTES GÉNÉRALES
L'ENTREPRENEUR ET LE RESPONSABLE DE CHANTIER DEVRONT, AVANT DE COMMENCER TOUT TRAVAIL,
VÉRIFIER LES DIMENSIONS DES DESSINS ET LES CONDITIONS EXISTANTES SUR LE CHANTIER ET SERONT TENUS D'AVISER L'INGÉNIEUR CIVIL DE TOUTES DIVERGENCES OU OMISSIONS.
LES PLANS DE L'INGÉNIEUR CIVIL ET DE L'ARCHITECTE PAYSAGISTE DOIVENT ÊTRE LUS DE FAÇON COMPLÉMENTAIRE. EN CAS DE CONFLIT L'ENTREPRENEUR ET LE RESPONSABLE DE CHANTIER DEVRONT AVISER LES CONSULTANTS CONCERNÉS.

NOTE 1
L'ENTREPRENEUR DOIT S'ASSURER DE COORDONNER TOUS LES NIVEAUX DES RADIERS DES BRANCHEMENTS DE SERVICES DU BÂTIMENT ET LEURS LOCALISATIONS AVEC LES PLANS DE L'INGÉNIEUR MÉCANIQUE.

01	20XX-XX-XX	ÉMIS POUR XXXX

émissions et révisions

sceau

projet

titre

échelle **date**	**dessiné** **vérifié**

contrat	**plan no**

projet: AMÉNAGEMENT
contrat:

1332 rue Beaubien est,
Montréal (Québec) H2G 1N5
Téléphone: 514-273-4272
www.mlacharlebois.com

FICHIER: 1787-GC-00_Superficie.dwg
IMPR.: 21 Mai 2026 - 9:03am
REPERTOIRE: H:\ENTREPRISES\MHA\GENERAL\Land Projects R2\1787\Travail\